NOTE:
THE SHADED AREAS SHOWN ON THE INTERIOR ELEVATIONS INDICATE ACCENT PAINT. COLORS TO BE SELECTED DURING THE SHOP DRAWING PHASE.

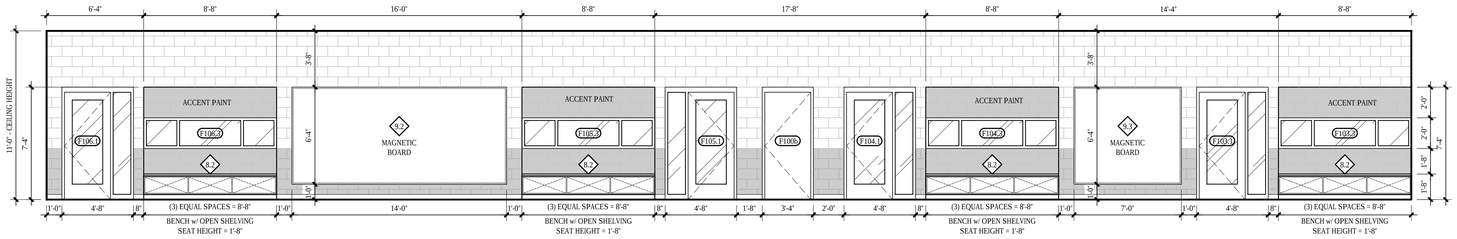

01 A6.0
Corridor F100
INTERIOR ELEVATION
Scale: 1/4" = 1'-0"

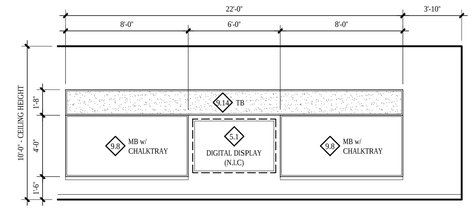

02 A6.0
TYPICAL Preschool Classroom
INTERIOR ELEVATION
Scale: 1/4" = 1'-0"

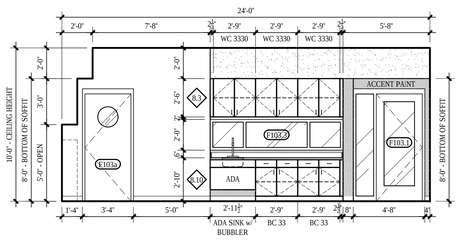

03 A6.0
Preschool Classroom
INTERIOR ELEVATION
Scale: 1/4" = 1'-0"

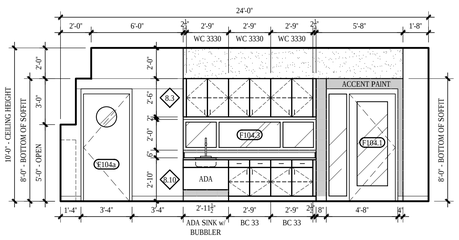

04 A6.0
Preschool Classroom
INTERIOR ELEVATION
Scale: 1/4" = 1'-0"

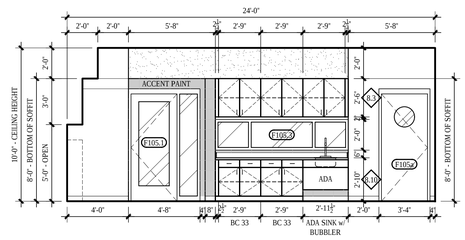

05 A6.0
Preschool Classroom
INTERIOR ELEVATION
Scale: 1/4" = 1'-0"

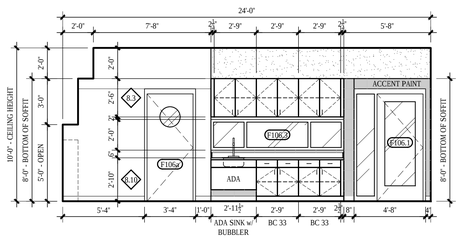

06 A6.0
Preschool Classroom F106
INTERIOR ELEVATION
Scale: 1/4" = 1'-0"

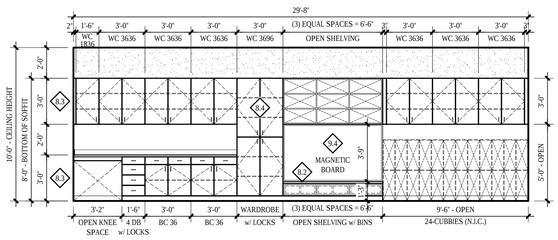

07 A6.0
Preschool Classroom
INTERIOR ELEVATION
Scale: 1/4" = 1'-0"

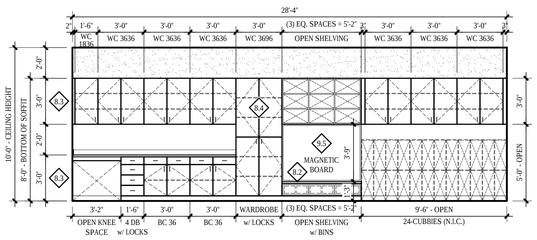

A6.0
Preschool Classroom
INTERIOR ELEVATION
Scale: 1/4" = 1'-0"

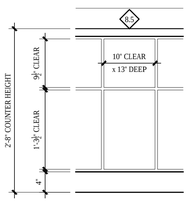

A6.0
Kindergarten Cubbies
ENLARGED ELEVATION
Scale: 1" = 1'-0"

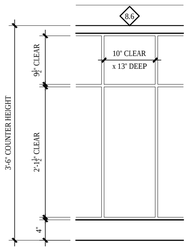

B A6.0
FMD Cubbies
ENLARGED ELEVATION
Scale: 1" = 1'-0"

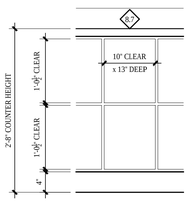

C A6.0
1st Grade Cubbies
ENLARGED ELEVATION
Scale: 1" = 1'-0"

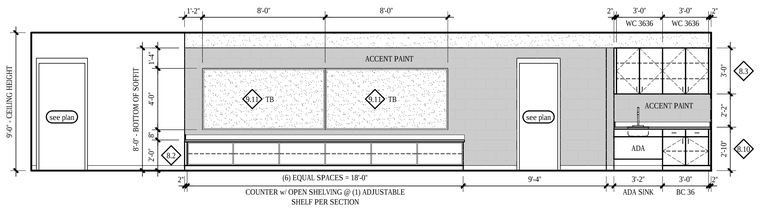

09 A6.0
Kindergarten Classroom
INTERIOR ELEVATION
Scale: 1/4" = 1'-0"

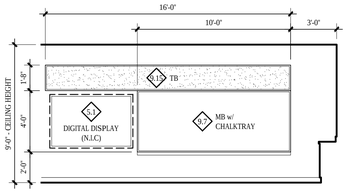

A6.0
Kindergarten : 1st Grade Classroom
INTERIOR ELEVATION
Scale: 1/4" = 1'-0"

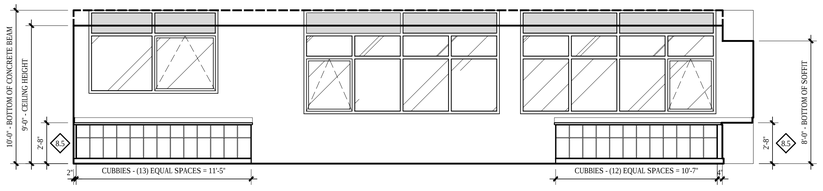

A6.0
Kindergarten Classroom
INTERIOR ELEVATION
Scale: 1/4" = 1'-0"

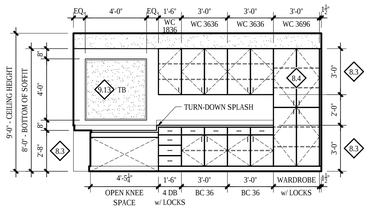

12 A6.0
Kindergarten Classroom
INTERIOR ELEVATION
Scale: 1/4" = 1'-0"

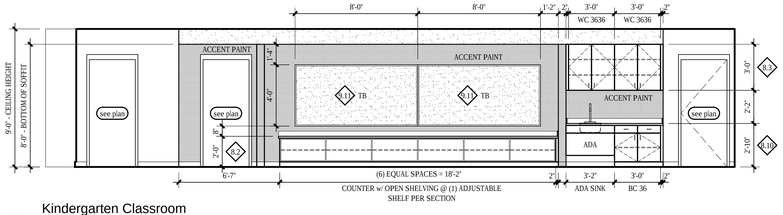

13 A6.0
Kindergarten Classroom
INTERIOR ELEVATION
Scale: 1/4" = 1'-0"

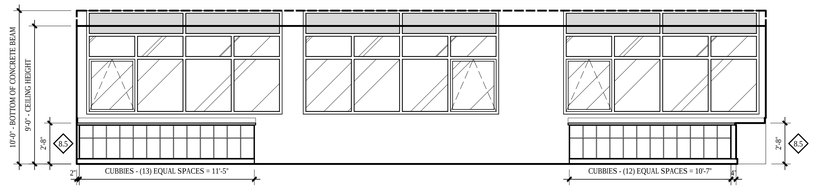

14 A6.0
Kindergarten Classroom
INTERIOR ELEVATION
Scale: 1/4" = 1'-0"

CONSTRUCTION DOCUMENTS

studio kremer architects
1231 S Shelby St. Louisville, KY 40203
TEL 502.499.1100 FAX 502.499.1101

DANVILLE INDEPENDENT SCHOOLS
ALL MEANS ALL

INTERIOR ELEVATIONS
Mary G. Hogsett Primary School Addition and Renovation
300 Waveland Avenue
Danville, Kentucky

BG# 17-292

DATE: 06.07.2018
DRAWN BY: AF | ska
CHECKED BY: mgh
REVISIONS:

ska# 2017-32

A6.0

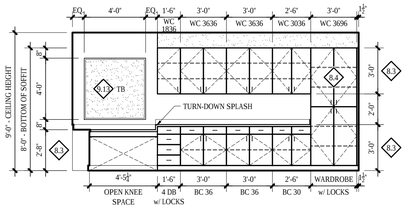

15 A6.1 Kindergarten Classroom
INTERIOR ELEVATION
Scale: 1/4" = 1'-0"

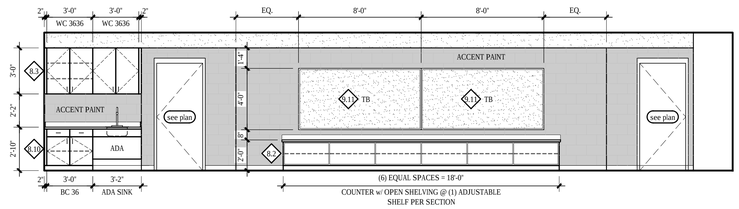

16 A6.1 Kindergarten Classroom
INTERIOR ELEVATION
Scale: 1/4" = 1'-0"

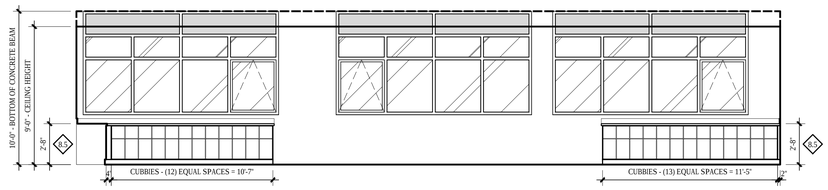

17 A6.1 Kindergarten Classroom
INTERIOR ELEVATION
Scale: 1/4" = 1'-0"

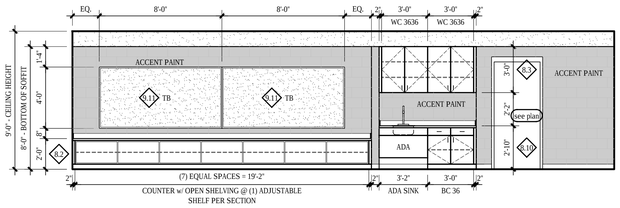

18 A6.1 Kindergarten Classroom
INTERIOR ELEVATION
Scale: 1/4" = 1'-0"

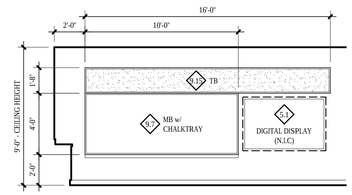

19 A6.1 Kindergarten : 1st Grade Classroom
INTERIOR ELEVATION
Scale: 1/4" = 1'-0"

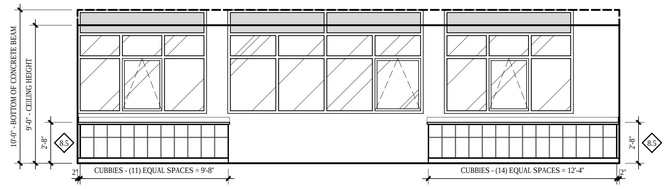

20 A6.1 Kindergarten Classroom
INTERIOR ELEVATION
Scale: 1/4" = 1'-0"

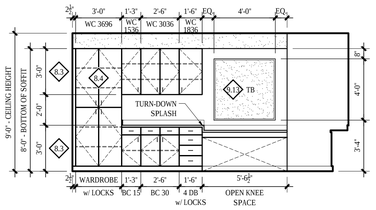

21 A6.1 Kindergarten Classroom
INTERIOR ELEVATION
Scale: 1/4" = 1'-0"

NOTE:
THE SHADED AREAS SHOWN ON THE INTERIOR ELEVATIONS INDICATE ACCENT PAINT. COLORS TO BE SELECTED DURING THE SHOP DRAWING PHASE.

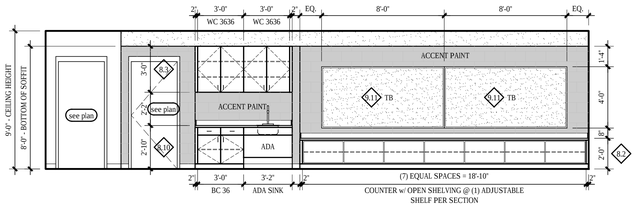

22 A6.1 Kindergarten Classroom
INTERIOR ELEVATION
Scale: 1/4" = 1'-0"

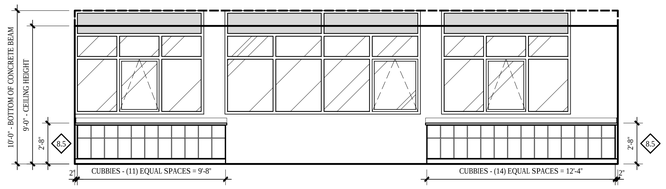

23 A6.1 Kindergarten Classroom
INTERIOR ELEVATION
Scale: 1/4" = 1'-0"

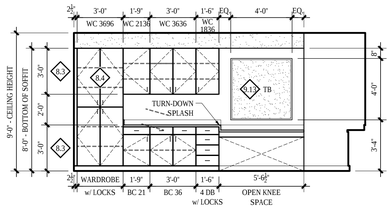

24 A6.1 Kindergarten Classroom
INTERIOR ELEVATION
Scale: 1/4" = 1'-0"

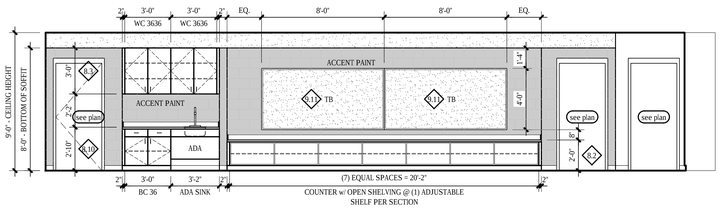

25 A6.1 Kindergarten Classroom
INTERIOR ELEVATION
Scale: 1/4" = 1'-0"

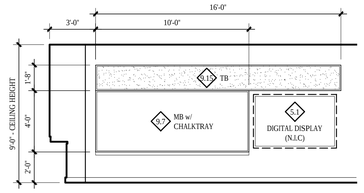

26 A6.1 Kindergarten : 1st Grade Classroom
INTERIOR ELEVATION
Scale: 1/4" = 1'-0"

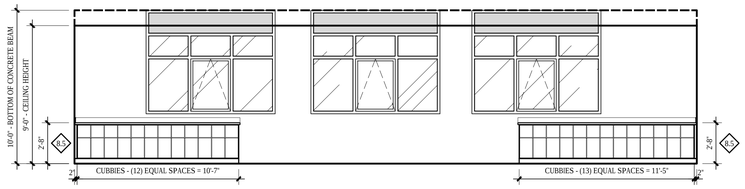

27 A6.1 Kindergarten Classroom
INTERIOR ELEVATION
Scale: 1/4" = 1'-0"

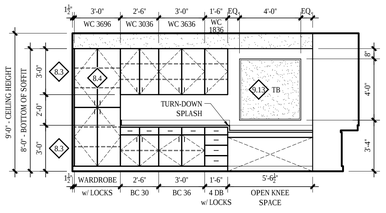

28 A6.1 Kindergarten Classroom
INTERIOR ELEVATION
Scale: 1/4" = 1'-0"

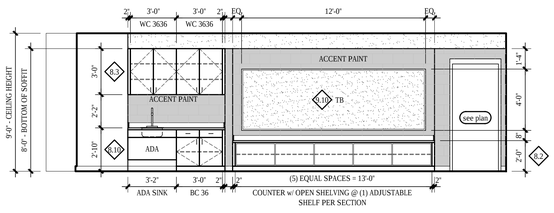

29 A6.1 1st Grade Classroom
INTERIOR ELEVATION
Scale: 1/4" = 1'-0"

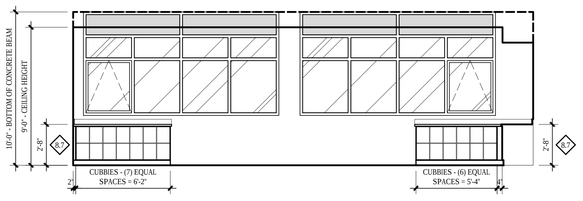

30 A6.1 1st Grade Classroom
INTERIOR ELEVATION
Scale: 1/4" = 1'-0"

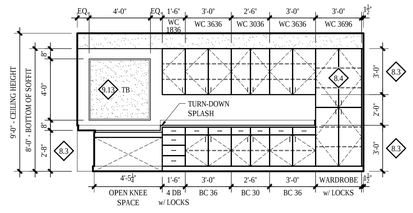

31 A6.1 1st Grade Classroom
INTERIOR ELEVATION
Scale: 1/4" = 1'-0"

CONSTRUCTION DOCUMENTS

studio kremer architects
1231 S Shelby St. Louisville, KY 40203
TEL 502.499.1100 FAX 502.499.1101

DANVILLE INDEPENDENT SCHOOLS
ALL MEANS ALL

INTERIOR ELEVATIONS

Mary G. Hogsett Primary School Addition and Renovation
300 Waveland Avenue
Danville, Kentucky

BG# 17-292

DATE: 06.07.2018
DRAWN BY: AF | ska
CHECKED BY: mgh
REVISIONS:

ska# 2017-32

A6.1