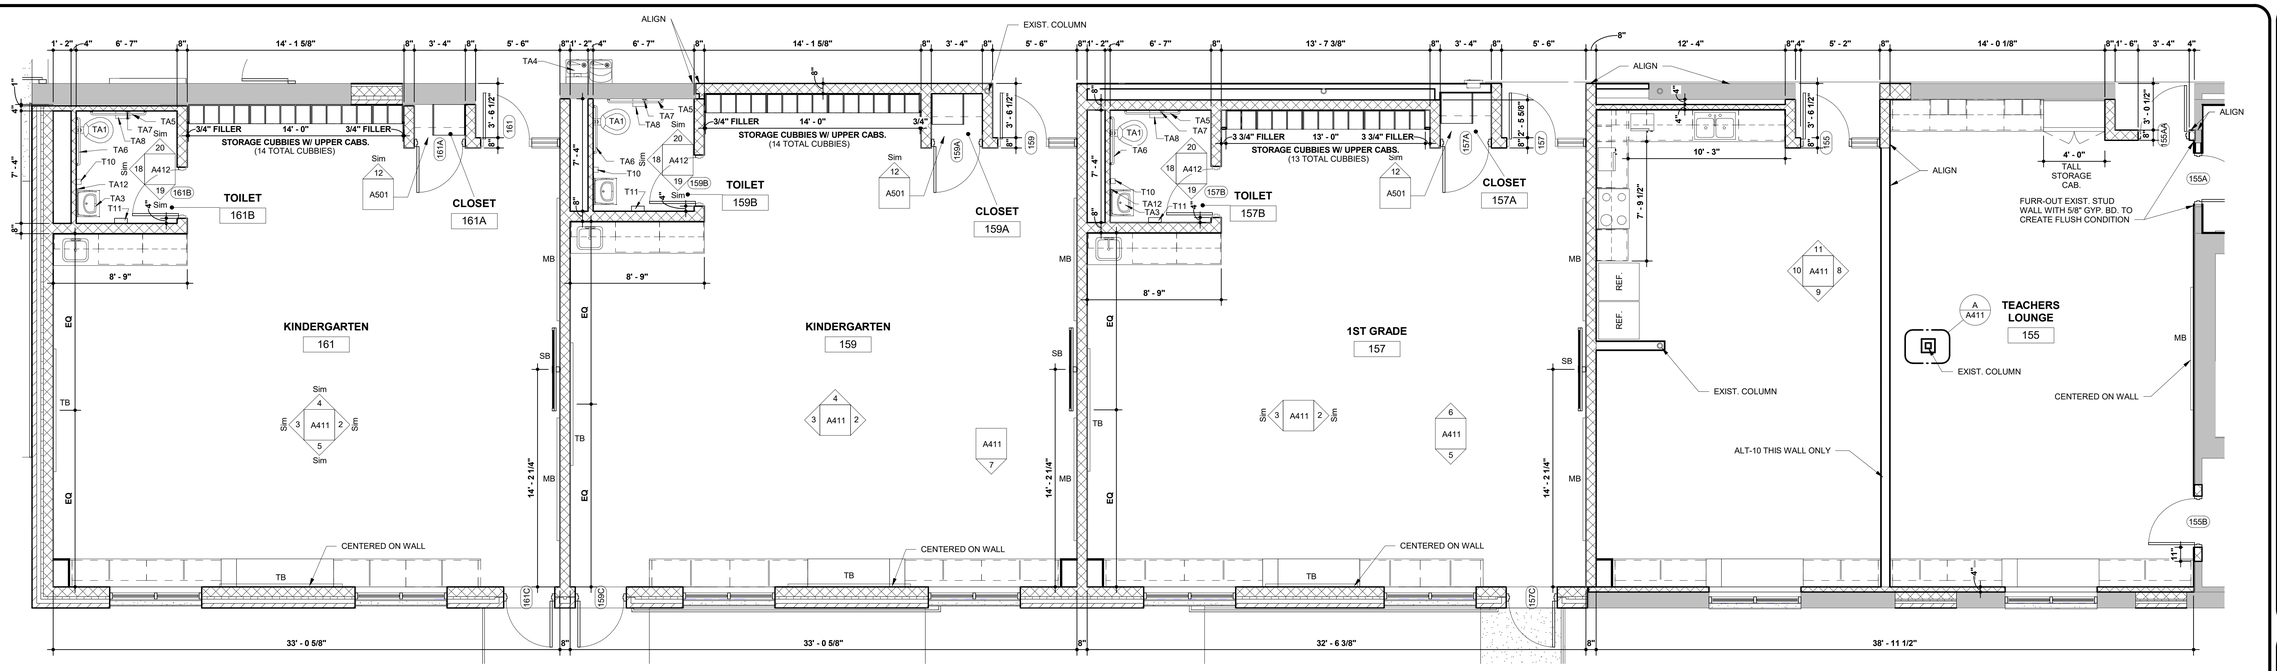

1 **ENLARGED PLAN AT KINDERGARTEN AND 1ST GRADES**
SCALE: 1/4" = 1'-0"

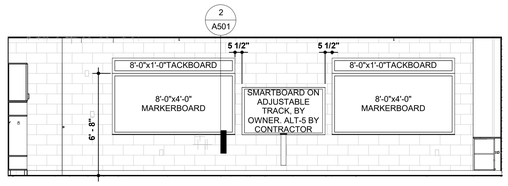

2 **KINDERGARTEN 159 N. ELEV.**
SCALE: 1/4" = 1'-0"
1ST GRADE 151 N.
KINDERGARTEN 157 N.
KINDERGARTEN 161 N.

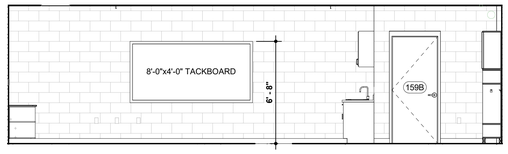

3 **KINDERGARTEN 159 S. ELEV.**
SCALE: 1/4" = 1'-0"
1ST GRADE 151 S.
KINDERGARTEN 157 S.
KINDERGARTEN 161 S.

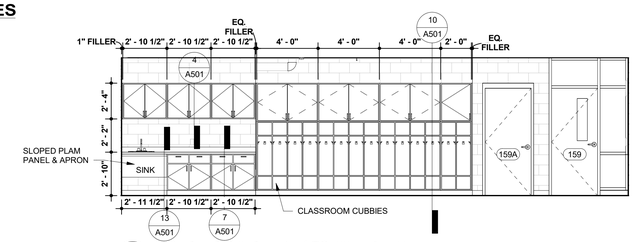

4 **KINDERGARTEN 159 W. ELEV.**
SCALE: 1/4" = 1'-0"
KINDERGARTEN 161 W.

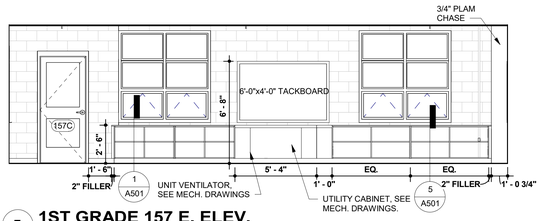

5 **1ST GRADE 157 E. ELEV.**
SCALE: 1/4" = 1'-0"
KINDERGARTEN 161 E.

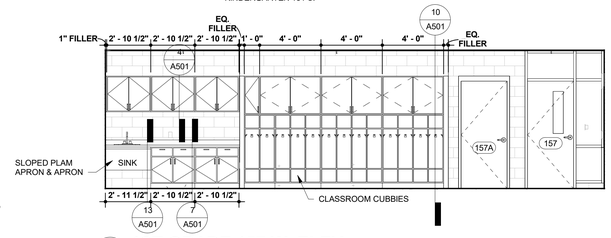

6 **1ST GRADE 157 W. ELEV.**
SCALE: 1/4" = 1'-0"

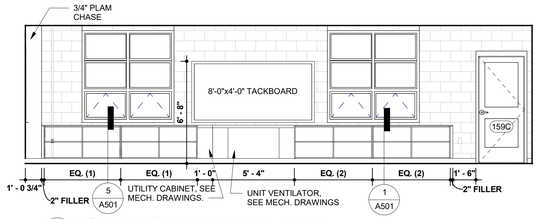

7 **KINDERGARTEN 159 E. ELEV.**
SCALE: 1/4" = 1'-0"

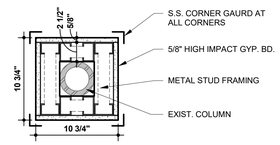

A **COLUMN COVER DETAIL**
SCALE: 1 1/2" = 1'-0"

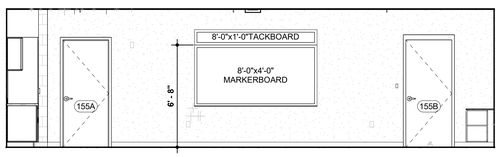

8 **TEACHERS LOUNGE 155 N. ELEV.**
SCALE: 1/4" = 1'-0"

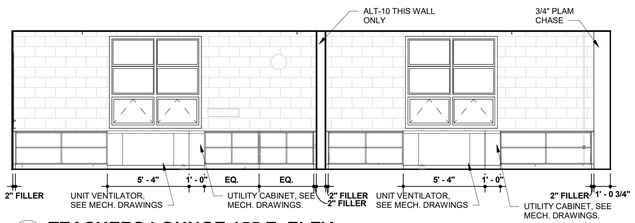

9 **TEACHERS LOUNGE 155 E. ELEV.**
SCALE: 1/4" = 1'-0"

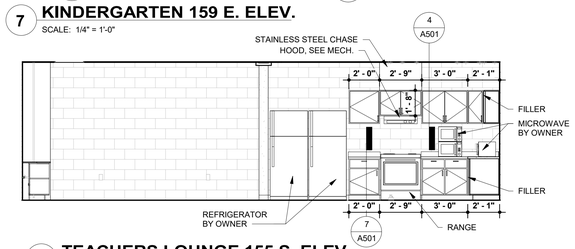

10 **TEACHERS LOUNGE 155 S. ELEV.**
SCALE: 1/4" = 1'-0"

PHASE 2 TACKBOARD/ MARKERBOARD QUANITY	
TACKBOARD/ MARKERBOARD SIZE	QUANITY
8'-0"x4'-0" MARKERBOARD	17
10'-0"x4'-0" MARKERBOARD	20
6'-0"x1'-0" TACKBOARD	1
6'-0"x4'-0" TACKBOARD	3
8'-0"x1'-0"TACKBOARD	17
8'-0"x4'-0" TACKBOARD	37
10'-0"x1'-0"TACKBOARD	21
10'-0"x4'-0" TACKBOARD	20
16'-0"x1'-0" TACKBOARD	12
20'-0"x1'-0" TACKBOARD	1

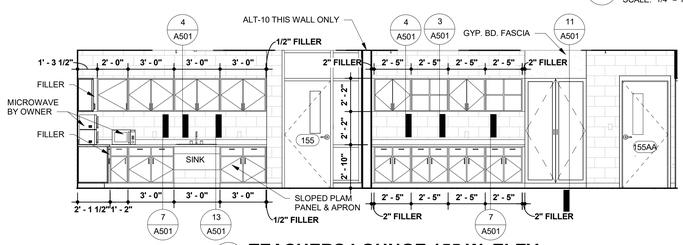

11 **TEACHERS LOUNGE 155 W. ELEV.**
SCALE: 1/4" = 1'-0"

HARVEY SCHOOL DISTRICT 152
MAYA ANGELOU ELEMENTARY SCHOOL-PH. 2
15748 PAGE AVENUE
HARVEY, ILLINOIS 60426

JMA Architects
16125 LaSalle Street
708-339-3900
FAX: 708-339-0949
South Holland, Illinois 60473
www.jmaarchitects.com

NO.	REVISIONS	DATE	BY

PROJECT NO. 2151 CHKD. JAM
DRAWN PMK ISSUED
DATE 09.16.22 FOR BIDDING

A411
SHEETS